



BITRA COLONY

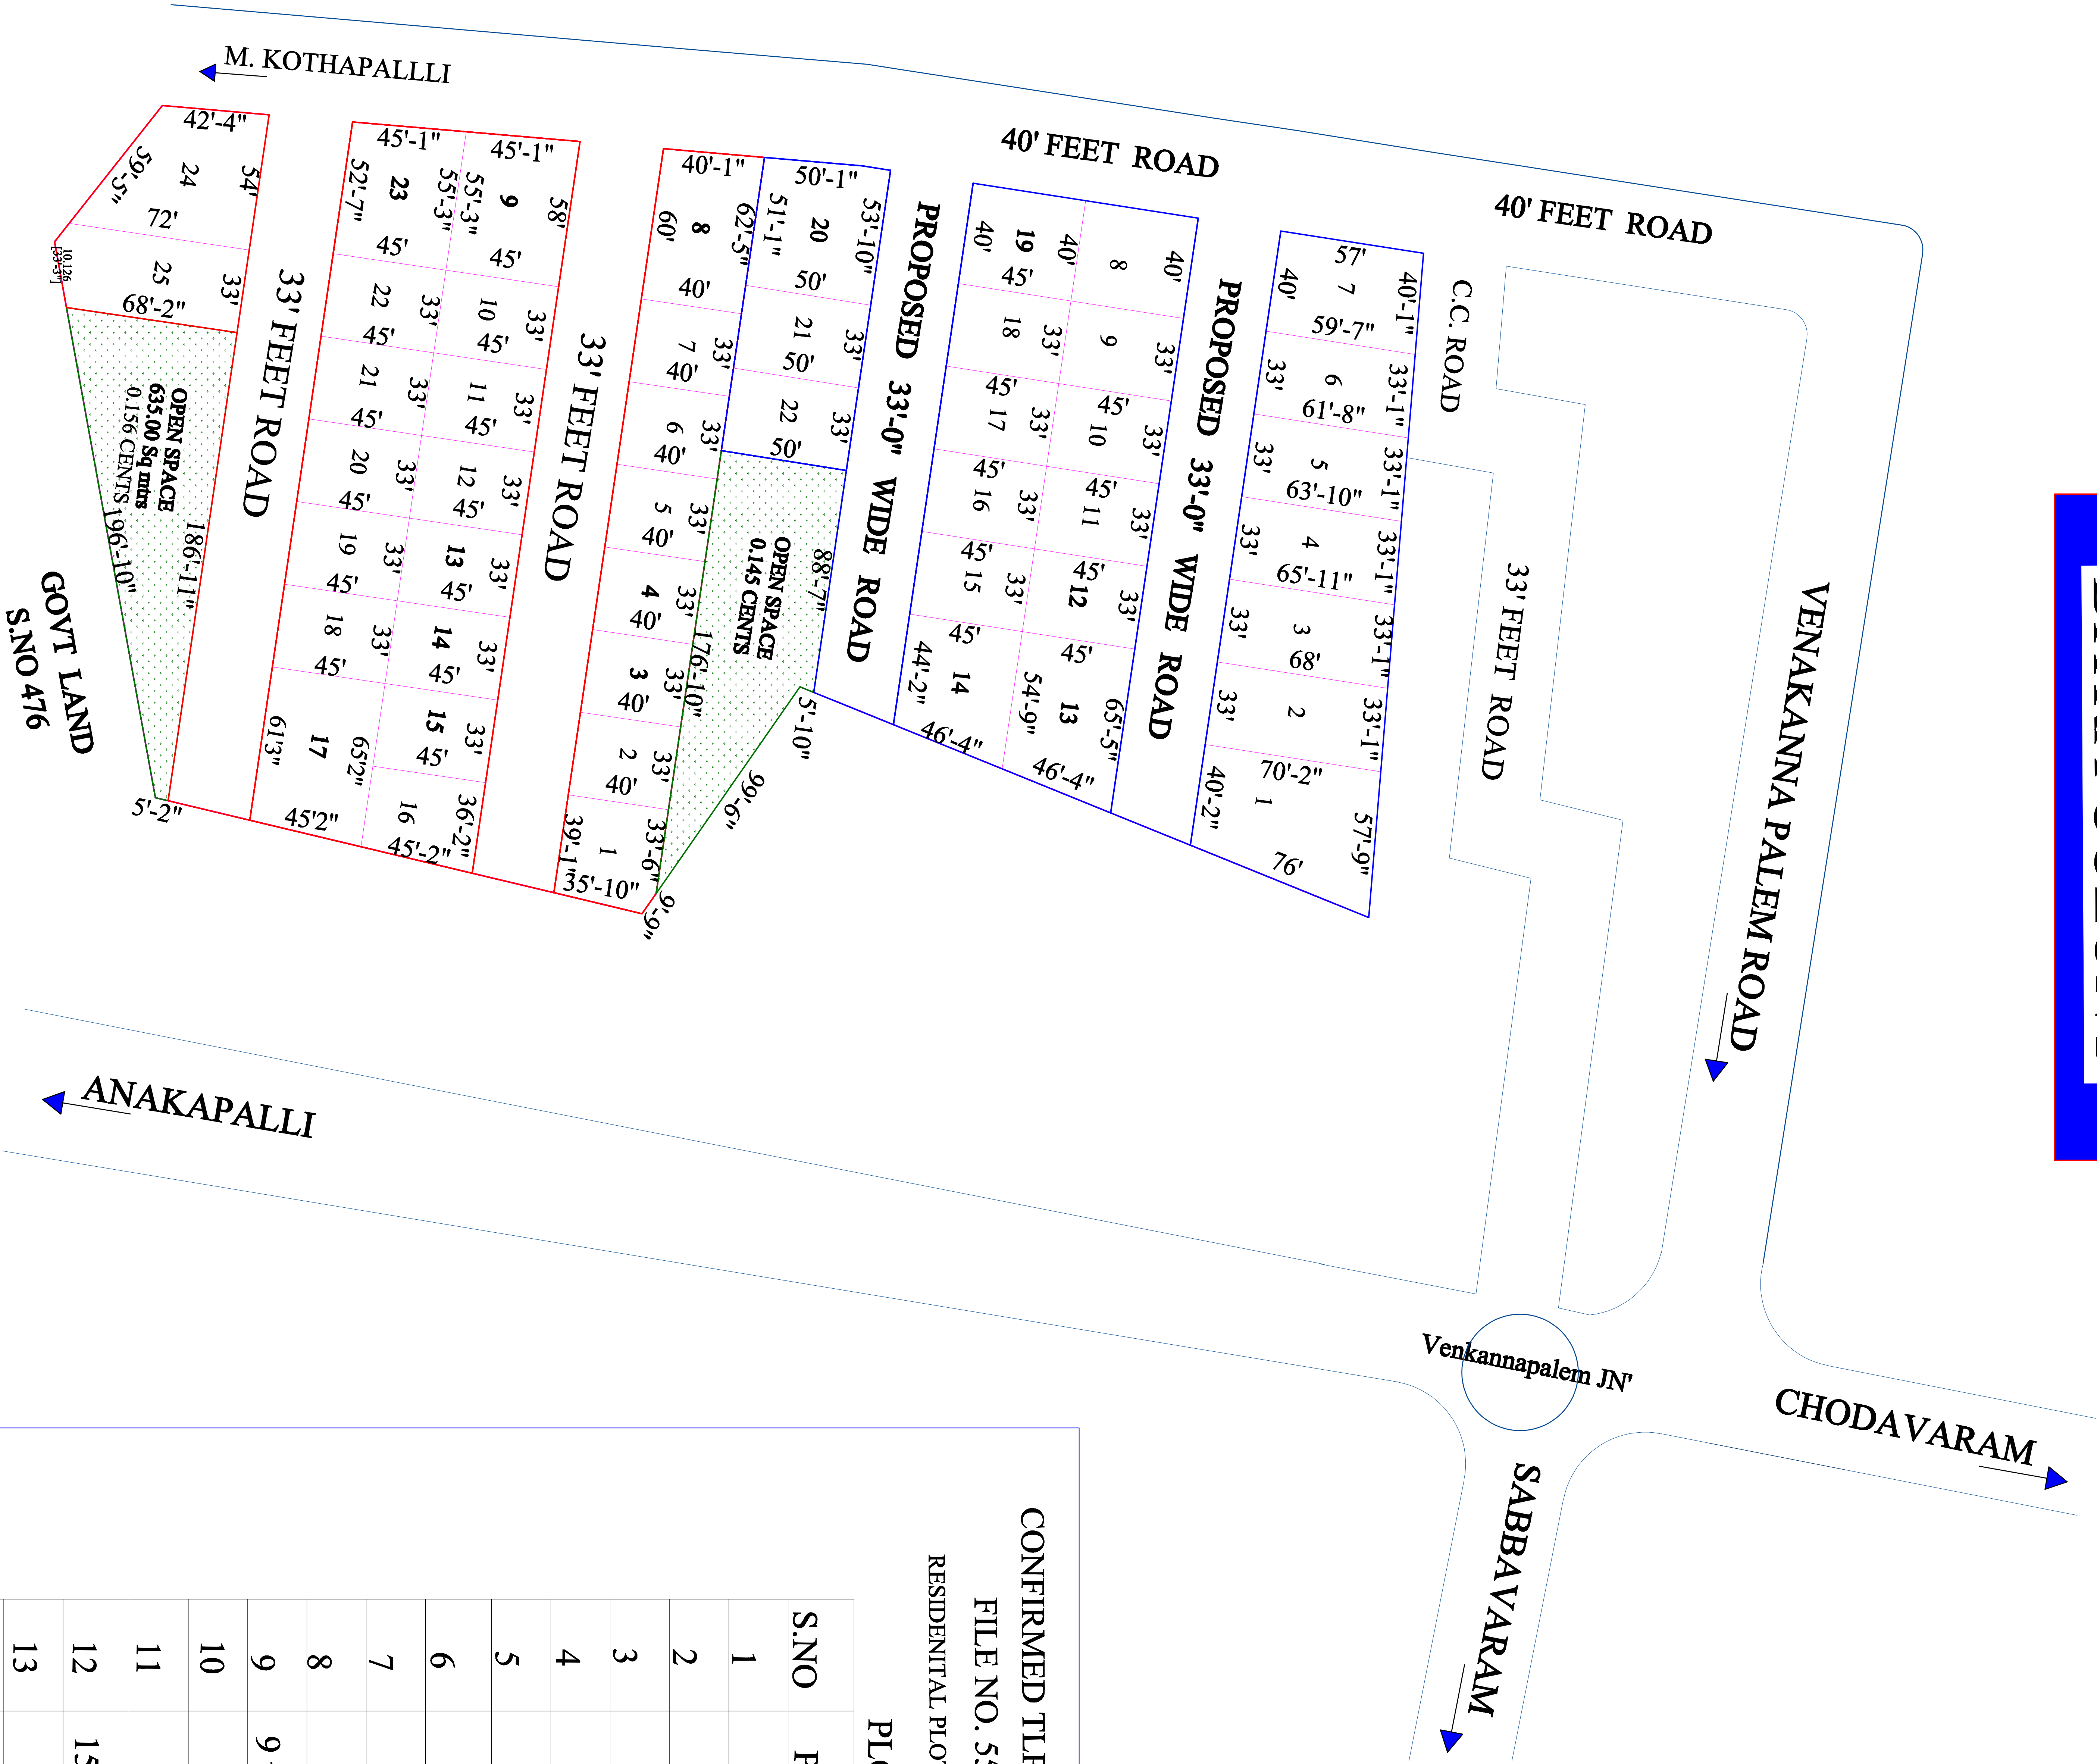

CONFIRMED TLP NO . 02/2019/DTCPO/VSP
FILE NO. 51/2019/DTCPO/VSP

VENKANNA PALEM GRAM PANCHATAT
TECHNICAL LAY - OUT PATTERN FOR
RESIDENTIAL PLOTS IN S.No's : 475/ 1Dp,
475/1E, 1F,1G,1H,
VENKANNA PALEM VILLAGE
Choodavaram Mandal, Visakhapatnam District.

CONFIRMED TLP NO . 03/2019/DTCPO/VSP
FILE NO. 55/2019/DTCPO/VSP
VENKANNA PALEM GRAM PANCHATAT
TECHNICAL LAY - OUT PATTERN FOR
RESIDENTIAL PLOTS IN S.No's : 475/1A, 1B,1C,1D(p),
VENKANNA PALEM VILLAGE
Choodavaram Mandal, Visakhapatnam District.

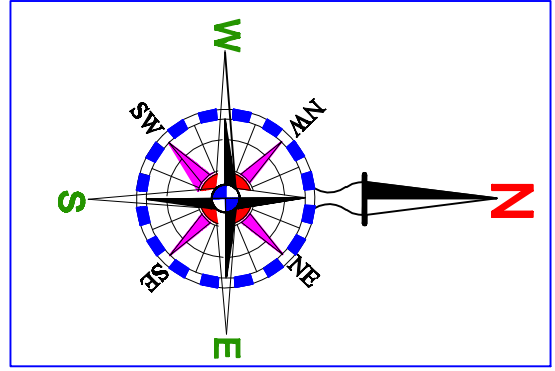

EXTRACT OF VENKANNA PALEM G.P
ALL DIMENSIONS ARE IN FEET
SCALE 1 : 1000
SITE UNDER REF

CONFIRMED TLP NO . 02/2019/DTCPO/VSP
FILE NO. 51/2019/DTCPO/VSP

RESIDENTIAL PLOTS IN S.No's : 475/ 1Dp,
475/1E, 1F,1G,1H,

PLOTED AREAS

S.NO	Plot NOS	Sq yds
1	1	179.196
2	2 to 7	146.666
3	8	272.066
4	9	283.272
5	10 to 15	165.000
6	16	170.836
7	17	316.043
8	18 to 22	165.024
9	23	269.674
10	24	232.260
11	25	267.030

CONFIRMED TLP NO . 03/2019/DTCPO/VSP
FILE NO. 55/2019/DTCPO/VSP

RESIDENTIAL PLOTS IN S.No's : 475/1A, 1B,1C,1D(p),

PLOTED AREAS

S.NO	Plot NOS	Sq yds
1	1	389.417
2	2	253.324
3	3	245.562
4	4	237.800
5	5	230.000
6	6	222.276
7	7	258.945
8	8	200.000
9	9 to 12	165.000
10	13	300.495
11	14	247.380
12	15 to 18	165.000
13	19	200.000
14	20	293.295
15	21 to 22	183.370